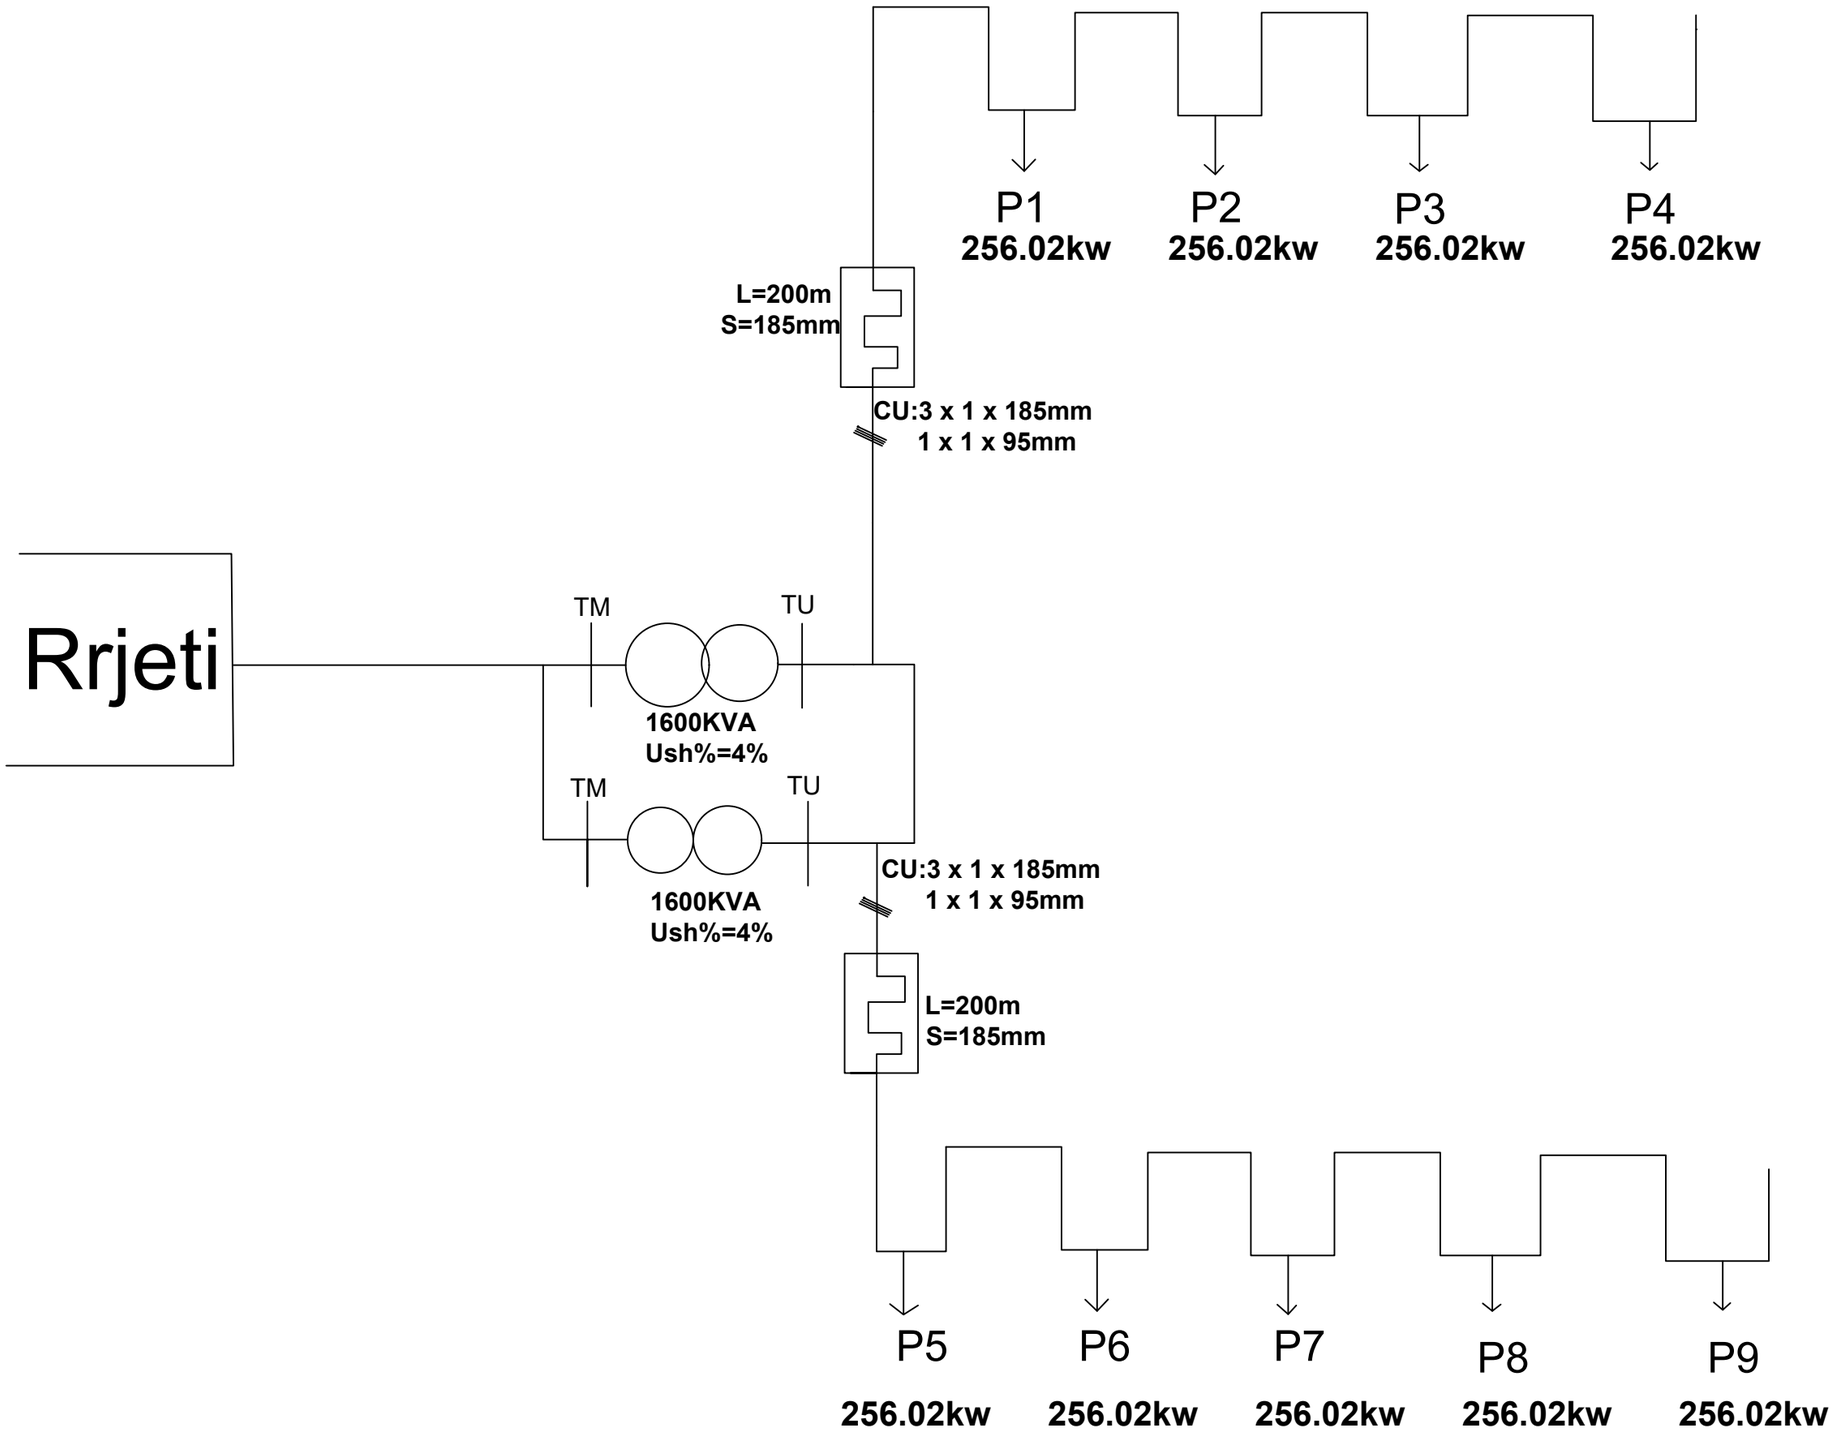

Rrjeti
TM
TU
1600KVA
Ush%=4%
TM
TU
1600KVA
Ush%=4%
L=200m
S=185mm
CU:3 x 1 x 185mm
1 x 1 x 95mm
CU:3 x 1 x 185mm
1 x 1 x 95mm
L=200m
S=185mm
P1
256.02kw
P2
256.02kw
P3
256.02kw
P4
256.02kw
P5
256.02kw
P6
256.02kw
P7
256.02kw
P8
256.02kw
P9
256.02kw